
ICF PACKAGE: Nudura ICF formwork and accessories are our supply. Raft and foundations AS PER THE ARCHITECTURAL DRAWINGS; joist ledgers by the engineer. Floors, stairs, partitions, roof and joinery are drawn as DESIGN ASSUMPTIONS for coordination - check by the relevant professional.

FOR APPROVAL - NOT FOR CONSTRUCTION


J1 5,044 O/A x 253 - 5 No.

ICF ledger -> GF spine (same ends: J2 4,987, J3 4,376, J4 4,006)

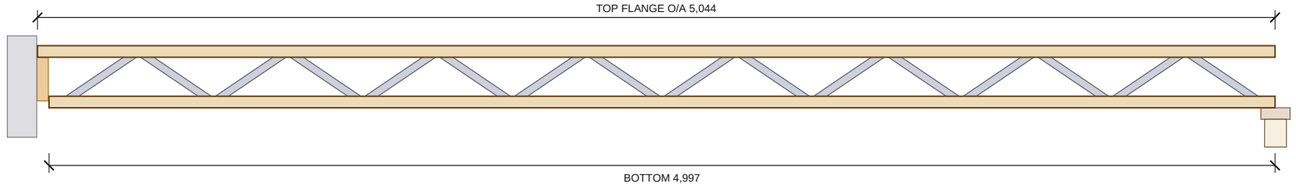


J5 3,122 O/A x 253 - 7 No.

GF spine -> ICF ledger (same ends: J6 2,084)

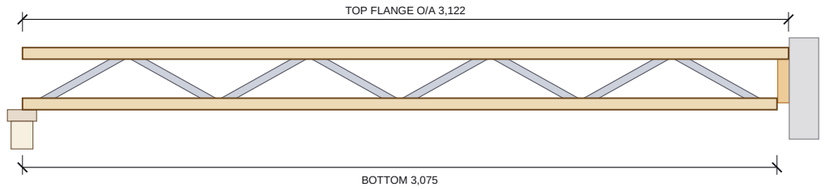


J7 1,640 O/A x 253 - 1 No.

GF spine -> stair trimmer (same ends: J8 1,028, J9 971)

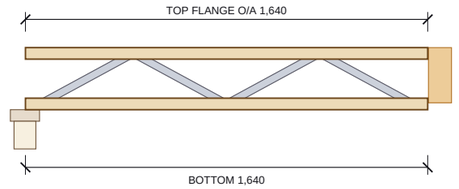


Elevations 1:25 (ICF ledger / GF spine head / stair trimmer at each end shown for context)

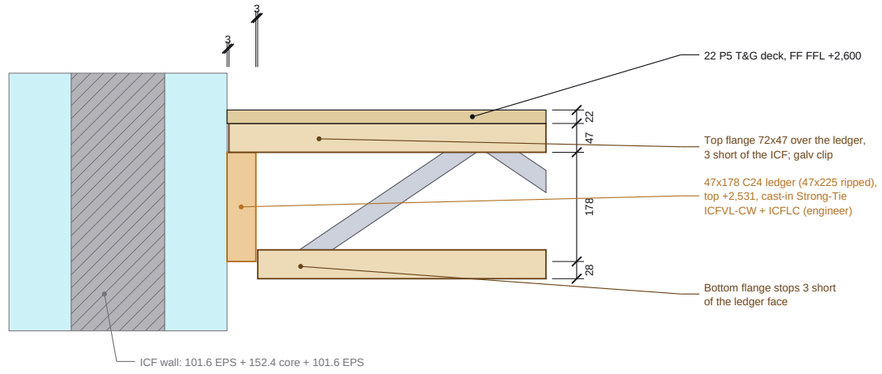

TOP-HUNG BEARING ON CUT-DOWN LEDGER

Scale 1:10 | typical at the ICF walls

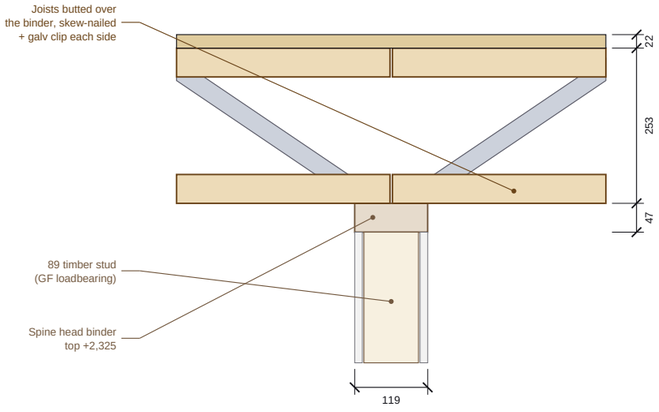

BEARING ON THE GF LOADBEARING SPINE

Scale 1:10 | GF spine G8-G12-G2-G7 (engineer to confirm)

JOIST TYPES

JOIST SCHEDULE

Type	O/A	Bottom	Depth	Flanges	Qty
J1	5,044	4,997	253	72x47	5
J2	4,987	4,940	253	72x47	1
J3	4,376	4,329	253	72x47	1
J4	4,006	3,959	253	72x47	7
J5	3,122	3,075	253	72x47	7
J6	2,084	2,037	253	72x47	3
J7	1,640	1,640	253	72x47	1
J8	1,028	1,028	253	72x47	1
J9	971	971	253	72x47	2
				Total	**28**

Qty = all units of the type. Metal-web joist equivalent, supplier to design.

WHERE USED (ENDS ALONG +X)

Type	Location
J1	ICF ledger to GF spine; U1
J2	ICF ledger to GF spine; U1
J3	ICF ledger to GF spine; U1
J4	ICF ledger to GF spine; U1
J5	GF spine to ICF ledger; U1
J6	GF spine to ICF ledger; U1
J7	GF spine to stair trimmer; U1
J8	GF spine to stair trimmer; U1
J9	GF spine to stair trimmer; U1

NOTES

1. DESIGN ASSUMPTION for coordination: 253 deep metal-web joists, e.g. Posi-Joist / Easi-Joist equivalent, 72 x 47 C24 (or stress-graded) flanges with galvanised V-web plates. The joist supplier designs the joists for the stated loads and confirms depth, web layout and spacing.
2. Loads (to be confirmed by the supplier): domestic floor, imposed 1.5 kN/m2 + lightweight stud partitions over, 22 Egger Protect P5 deck, plasterboard ceiling under. 600 c/c, spans onto the GF loadbearing spine.
3. Ends: TOP-HUNG at the ICF - top flange over the 47 x 178 C24 ledger to 3 short of the ICF face, bottom flange 3 short of the ledger, galv clip to the ledger; at the GF spine bearing on the head binder, butted over its centre; trimmed joists face-fix hung off the stair trimmer.
4. Web pattern shown is indicative (from the approval model); webs at the supplier's standard pitch.
5. Ogwen 5P4B (detached). Datum 0 = GF FFL. Architect: Beech Developments - BD0154-OGW rev A (JHG 28/10/26).

REVISIONS

REV	DATE	DESCRIPTION
P01	29.10.26	Approval issue

Nudura™ BuildEase

CLIENT	PROJECT
Beech Developments (NW) Ltd	Maes Y Felin, Glan Conwy - Ogwen

DRAWING TITLE

OGWEN - FLOOR JOIST PROFILES

Metal-web joist profiles (design assumption)

SCALE	SIZE	DATE
1:25 / 1:10	A3	29.10.26
DRAWN	**CHECKED**	**APPROVED**
TS		

STATUS	DRAWING No.	REV
FOR APPROVAL	ES26-020-OGW-FL-02	P01

Do not scale. All dimensions in mm. Check all dimensions on site.