

ICF PACKAGE: Nudura ICF formwork and accessories are our supply. Raft and foundations AS PER THE ARCHITECTURAL DRAWINGS; joist ledgers by the engineer. Floors, stairs, partitions, roof and joinery are drawn as DESIGN ASSUMPTIONS for coordination - check by the relevant professional.

FOR APPROVAL - NOT FOR CONSTRUCTION

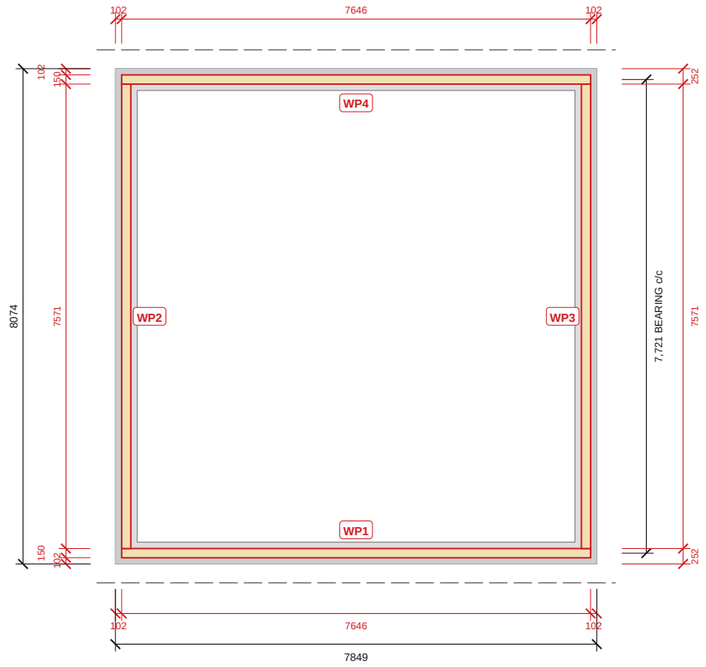

WALL PLATE SETTING-OUT PLAN

Scale 1:100 | dims from the OUTER ICF face; dashed = eaves line

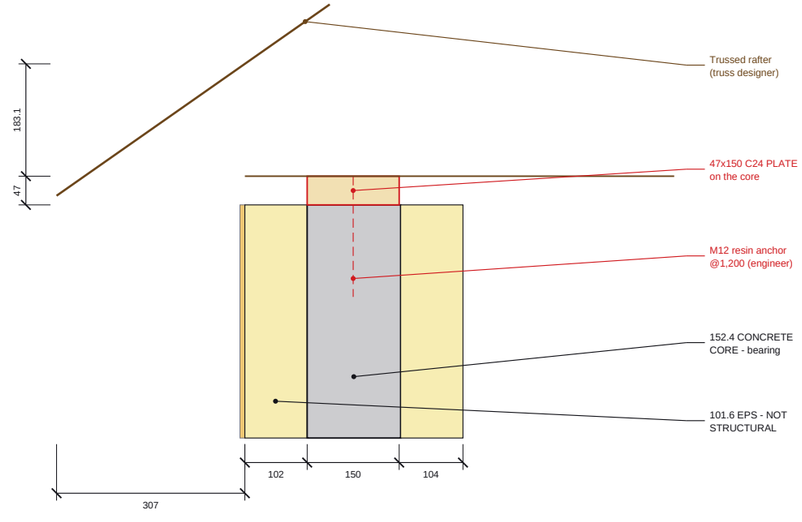

EAVES SECTION AT THE PLATE

Scale 1:10 | front / rear walls (see DT-03)

WALL PLATE SCHEDULE

47 X 150 C24 TREATED, TOP +5,076

Plate	Length	Runs	On the core
WP1	7,646	x 102 - 7,747	y 101.6 - 251.6
WP2	7,571	y 252 - 7,822	x 101.6 - 251.6
WP3	7,571	y 252 - 7,822	x 7597.4 - 7747.4
WP4	7,646	x 102 - 7,747	y 7822.4 - 7972.4

x from the left outer ICF face, y from the front outer ICF face.

BEARING

Item	mm
Plate centre from outer face	176.6
Span between plate centres (front-rear)	7,721
Outer ICF face to face	8,074
Heel at the outer face	183.1
Overhang beyond the outer face	307

NOTES

1. FOR THE TRUSS DESIGNER: the external walls are Nudura 6in XR35 insulated concrete formwork - 101.6 EPS foam / 152.4 reinforced concrete core / 101.6 EPS foam (355.6 overall), rendered outside (Dryvit ICF 500), lined inside.
2. The EPS is formwork and insulation only - it is NOT STRUCTURAL and must carry no load. The trusses bear on the 47 x 150 C24 treated WALL PLATE, which sits on the CONCRETE CORE ONLY: 101.6 to 251.6 in from the outer ICF face.
3. Core top +5,029 above GF FFL; plate top (truss bearing) +5,076. All dimensions are from the OUTER face of the ICF (the render adds 8).
4. Plate fixing: M12 resin anchors into the core @ 1,200 max, 300 from each end and each side of every joint - DESIGN ASSUMPTION, engineer to confirm. Truss clips to the plate and restraint straps by the truss designer.
5. Heel 183.1 (plate top to rafter top at the outer ICF face); eaves overhang 307 beyond the outer ICF face (tiles 382). Pitch 35 deg, hip ends 40 deg.
6. HIPPED ROOF: plates on all four walls - front and rear full length, the side plates between them.
7. Ogwen 5P4B (detached). Datum 0 = GF FFL. Architect: Beech Developments - BD0154-OGW rev A (JHG 28/10/26).

REVISIONS

REV	DATE	DESCRIPTION
P01	29.10.26	Approval issue

Nudura™ BuildEase

CLIENT	PROJECT
Beech Developments (NW) Ltd	Maes Y Felin, Glan Conwy - Ogwen

DRAWING TITLE

OGWEN - WALL PLATE SETTING-OUT FOR THE TRUSS DESIGNER

SCALE	SIZE	DATE
AS SHOWN	A3	29.10.26
DRAWN: TS	CHECKED	APPROVED

STATUS	DRAWING No.	REV
FOR APPROVAL	ES26-020-OGW-RF-00	P01

Do not scale. All dimensions in mm. Check all dimensions on site.