

ICF PACKAGE: Nudura ICF formwork and accessories are our supply. Raft and foundations AS PER THE ARCHITECTURAL DRAWINGS; joist ledgers by the engineer. Floors, stairs, partitions, roof and joinery are drawn as DESIGN ASSUMPTIONS for coordination - check by the relevant professional.

FOR APPROVAL - NOT FOR CONSTRUCTION

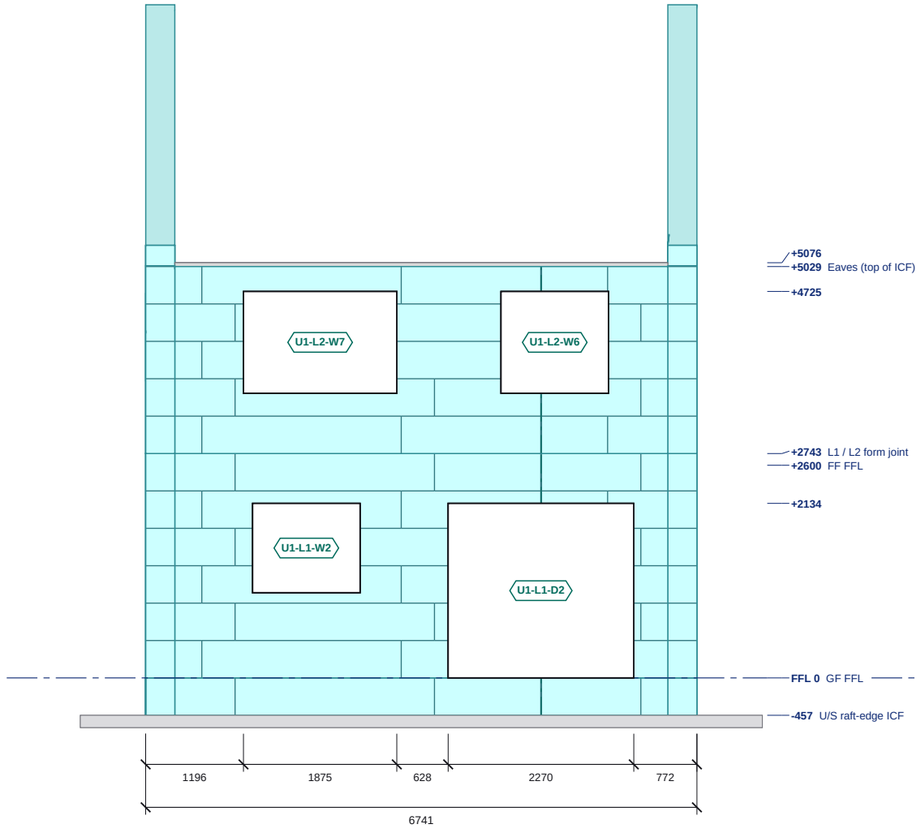

REAR ELEVATION

Scale 1:75 @ A3 | Levels above GF FFL; sills and heads in the schedule

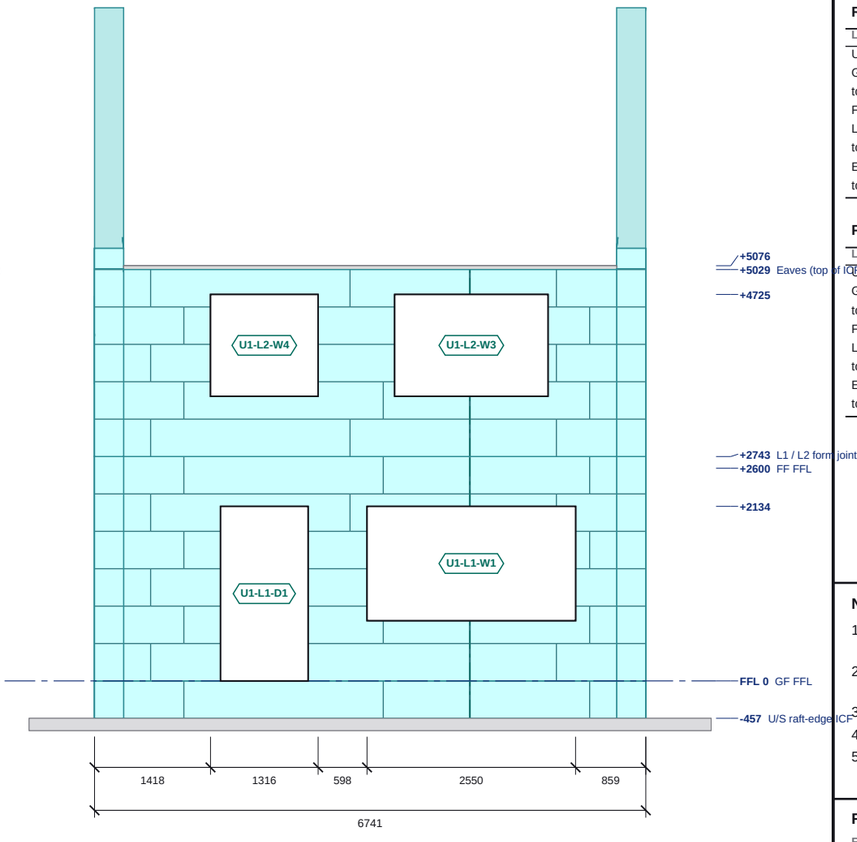

FRONT ELEVATION

Scale 1:75 @ A3 | Levels above GF FFL; sills and heads in the schedule

0 1 2 3 4m

ICF external EPS face
Block course joint
Stack joint
Roof build-up (slab / earth / sedum)

Do not scale. All dimensions in millimetres, levels in metres from GF FFL. Check all dimensions on site.

ELEVATION SCHEDULES

REAR ELEVATION: OPENINGS

Ref	Width	Height	Sill	Head	Lintel
U1-L1-D2	2270	2134	0	+2134	-
U1-L1-W2	1315	1092	+1042	+2134	-
U1-L2-W6	1315	1244	+3480	+4724	-
U1-L2-W7	1875	1244	+3480	+4724	-

Structural openings in the ICF; sill and head above GF FFL.

FRONT ELEVATION: OPENINGS

Ref	Width	Height	Sill	Head	Lintel
U1-L1-D1	1070	2134	0	+2134	-
U1-L1-W1	2550	1397	+737	+2134	-
U1-L2-W4	1315	1244	+3480	+4724	-
U1-L2-W3	1875	1244	+3480	+4724	-

Structural openings in the ICF; sill and head above GF FFL.

REAR ELEVATION: LEVELS

Level	FFL
U/S raft-edge ICF	-457
GF FFL	0
top of ICF	+2134
FF FFL	+2600
L1 / L2 form joint	+2743
top of ICF	+4725
Eaves (top of ICF)	+5029
top of roof build-up	+5076

FRONT ELEVATION: LEVELS

Level	FFL
U/S raft-edge ICF	-457
GF FFL	0
top of ICF	+2134
FF FFL	+2600
L1 / L2 form joint	+2743
top of ICF	+4725
Eaves (top of ICF)	+5029
top of roof build-up	+5076

NOTES

1. ICF: Nudura 6" XR35, 101.6 EPS + 152.4 core + 101.6 EPS = 355.6. External EPS face shown with the block course joints, vertical block joints and stack joints as populated.
2. Levels above GF FFL. Openings are structural openings in the ICF; glazing, doors, render and finishes by others, not shown.
3. Roof build-up shown as modelled.
4. See ES26-020-POW-GA-01 for plan setting out, lintels and steel.
5. Powys (detached), plot 14, building B05. Datum 0 = GF FFL. Architect: Beech Developments - BD0154-POW rev A (JHG 26/10/26).

REVISIONS

REV	DATE	DESCRIPTION
P01	29.10.26	Approval issue

Nudura™ BuildEase

CLIENT	PROJECT
Beech Developments (NW) Ltd	Maes Y Felin, Glan Conwy - Powys

DRAWING TITLE

NORTH AND SOUTH ELEVATIONS

ICF elevations with openings, levels and roof build-up

SCALE	SIZE	DATE
1:75	A3	29.10.26
DRAWN	CHECKED	APPROVED
TS		

STATUS	DRAWING No.	REV
FOR APPROVAL	ES26-020-POW-EL-01	P01