
ICF PACKAGE: Nudura ICF formwork and accessories are our supply. Raft and foundations AS PER THE ARCHITECTURAL DRAWINGS; joist ledgers by the engineer. Floors, stairs, partitions, roof and joinery are drawn as DESIGN ASSUMPTIONS for coordination - check by the relevant professional.

FOR APPROVAL - NOT FOR CONSTRUCTION


J1 6,023 O/A x 253 - 6 No.

ICF ledger -> ICF ledger

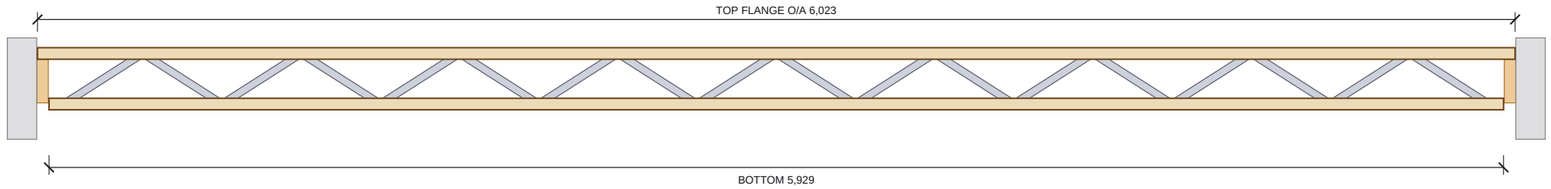


J2 3,617 O/A x 253 - 11 No.

GF spine -> ICF ledger

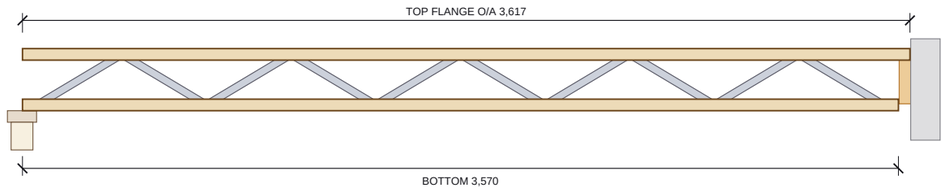


J3 2,402 O/A x 253 - 7 No.

ICF ledger -> GF spine

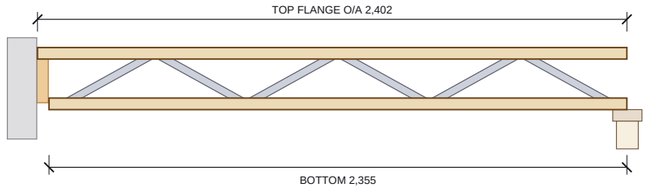


J4 1,288 O/A x 253 - 4 No.

stair trimmer -> GF spine

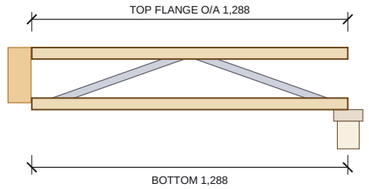


Elevations 1:25 (ICF ledger / GF spine head / stair trimmer at each end shown for context)

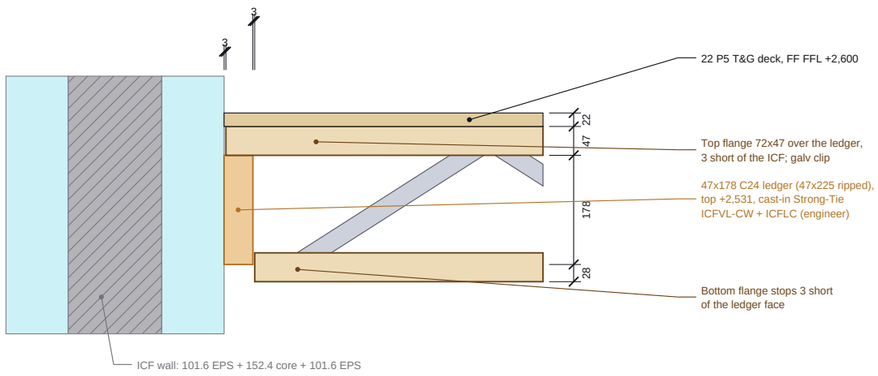

TOP-HUNG BEARING ON CUT-DOWN LEDGER

Scale 1:10 | typical at the ICF walls

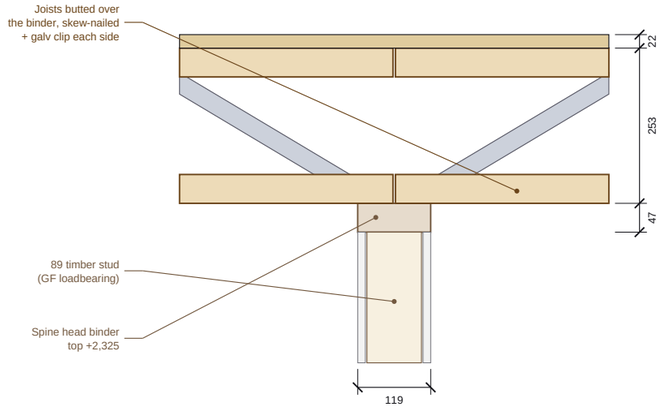

BEARING ON THE GF LOADBEARING SPINE

Scale 1:10 | GF spine G7 (engineer to confirm)

JOIST TYPES

JOIST SCHEDULE

Type	O/A	Bottom	Depth	Flanges	Qty
J1	6,023	5,929	253	72x47	6
J2	3,617	3,570	253	72x47	11
J3	2,402	2,355	253	72x47	7
J4	1,288	1,288	253	72x47	4
				Total	**28**

Qty = all units of the type. Metal-web joist equivalent, supplier to design.

WHERE USED (ENDS ALONG +X)

Type	Location
J1	ICF ledger to ICF ledger; U1
J2	GF spine to ICF ledger; U1
J3	ICF ledger to GF spine; U1
J4	stair trimmer to GF spine; U1

NOTES

1. DESIGN ASSUMPTION for coordination: 253 deep metal-web joists, e.g. Posi-Joist / Easi-Joist equivalent, 72 x 47 C24 (or stress-graded) flanges with galvanised V-web plates. The joist supplier designs the joists for the stated loads and confirms depth, web layout and spacing.
2. Loads (to be confirmed by the supplier): domestic floor, imposed 1.5 kN/m2 + lightweight stud partitions over, 22 Egger Protect P5 deck, plasterboard ceiling under. 600 c/c, spans onto the GF loadbearing spine.
3. Ends: TOP-HUNG at the ICF - top flange over the 47 x 178 C24 ledger to 3 short of the ICF face, bottom flange 3 short of the ledger, galv clip to the ledger; at the GF spine bearing on the head binder, butted over its centre; trimmed joists face-fix hung off the stair trimmer.
4. Web pattern shown is indicative (from the approval model); webs at the supplier's standard pitch.
5. Powys (detached), plot 14, building B05. Datum 0 = GF FFL. Architect: Beech Developments - BD0154-POW rev A (JHG 26/10/26).

REVISIONS

REV	DATE	DESCRIPTION
P01	29.10.26	Approval issue

Nudura™ BuildEase

CLIENT	PROJECT
Beech Developments (NW) Ltd	Maes Y Felin, Glan Conwy - Powys

DRAWING TITLE

POWYS - FLOOR JOIST PROFILES

Metal-web joist profiles (design assumption)

SCALE	SIZE	DATE
1:25 / 1:10	A3	29.10.26
DRAWN	CHECKED	APPROVED
TS		

STATUS	DRAWING No.	REV
FOR APPROVAL	ES26-020-POW-FL-02	P01

Do not scale. All dimensions in mm. Check all dimensions on site.