

ICF PACKAGE: Nudura ICF formwork and accessories are our supply. Raft and foundations AS PER THE ARCHITECTURAL DRAWINGS; joist ledgers by the engineer. Floors, stairs, partitions, roof and joinery are drawn as DESIGN ASSUMPTIONS for coordination - check by the relevant professional.

FOR APPROVAL - NOT FOR CONSTRUCTION

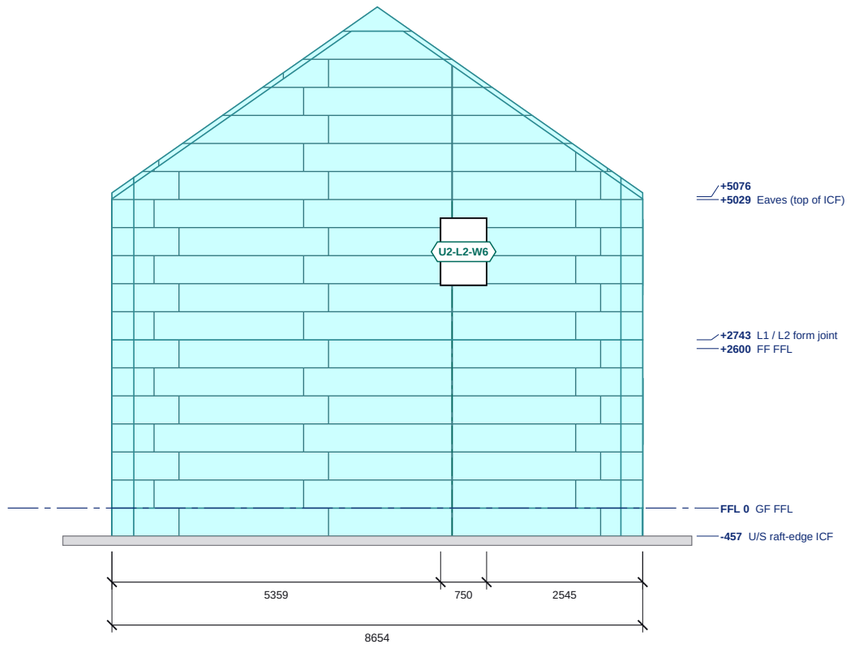

RIGHT SIDE ELEVATION

Scale 1:100 @ A3 | Levels above GF FFL; sills and heads in the schedule

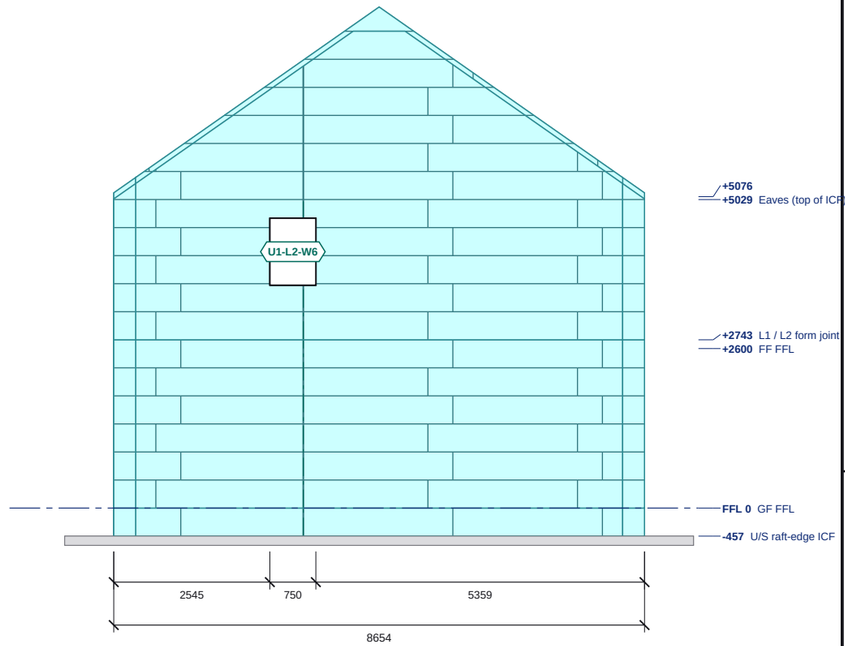

LEFT SIDE ELEVATION

Scale 1:100 @ A3 | Levels above GF FFL; sills and heads in the schedule



ICF external EPS face
Block course joint
Stack joint
Roof build-up (slab / earth / sedum)

ELEVATION SCHEDULES

RIGHT SIDE ELEVATION: OPENINGS

Ref	Width	Height	Sill	Head	Lintel
U2-L2-W6	750	1092	+3633	+4724	-

Structural openings in the ICF; sill and head above GF FFL.

LEFT SIDE ELEVATION: OPENINGS

Ref	Width	Height	Sill	Head	Lintel
U1-L2-W6	750	1092	+3633	+4724	-

Structural openings in the ICF; sill and head above GF FFL.

RIGHT SIDE ELEVATION: LEVELS

Level	FFL
U/S raft-edge ICF	-457
GF FFL	0
FF FFL	+2600
L1 / L2 form joint	+2743
Eaves (top of ICF)	+5029
top of roof build-up	+5076

LEFT SIDE ELEVATION: LEVELS

Level	FFL
U/S raft-edge ICF	-457
GF FFL	0
FF FFL	+2600
L1 / L2 form joint	+2743
Eaves (top of ICF)	+5029
top of roof build-up	+5076

NOTES

1. ICF: Nudura 6" XR35, 101.6 EPS + 152.4 core + 101.6 EPS = 355.6; 6" Std, 66.7 EPS + 152.4 core + 66.7 EPS = 285.8. External EPS face shown with the block course joints, vertical block joints and stack joints as populated.
2. Levels above GF FFL. Openings are structural openings in the ICF; glazing, doors, render and finishes by others, not shown.
3. Roof build-up shown as modelled.
4. See ES26-020-3B4P-GA-01 for plan setting out, lintels and steel.
5. 3B4P (semi pair), plots 16-17, building B07. Datum 0 = GF FFL. Architect: Beech Developments - BD0154-3B4P rev A (JHG 26/10/26).

REVISIONS

REV	DATE	DESCRIPTION
P01	03.11.26	Approval issue

Nudura™ BuildEase

CLIENT	PROJECT
Beech Developments (NW) Ltd	Maes Y Felin, Glan Conwy - 3B4P

DRAWING TITLE

EAST AND WEST ELEVATIONS

ICF elevations with openings, levels and roof build-up

SCALE	SIZE	DATE
1:100	A3	03.11.26
DRAWN	CHECKED	APPROVED
TS		

STATUS	DRAWING No.	REV
FOR APPROVAL	ES26-020-3B4P-EL-02	P01

Do not scale. All dimensions in millimetres, levels in metres from GF FFL. Check all dimensions on site.